

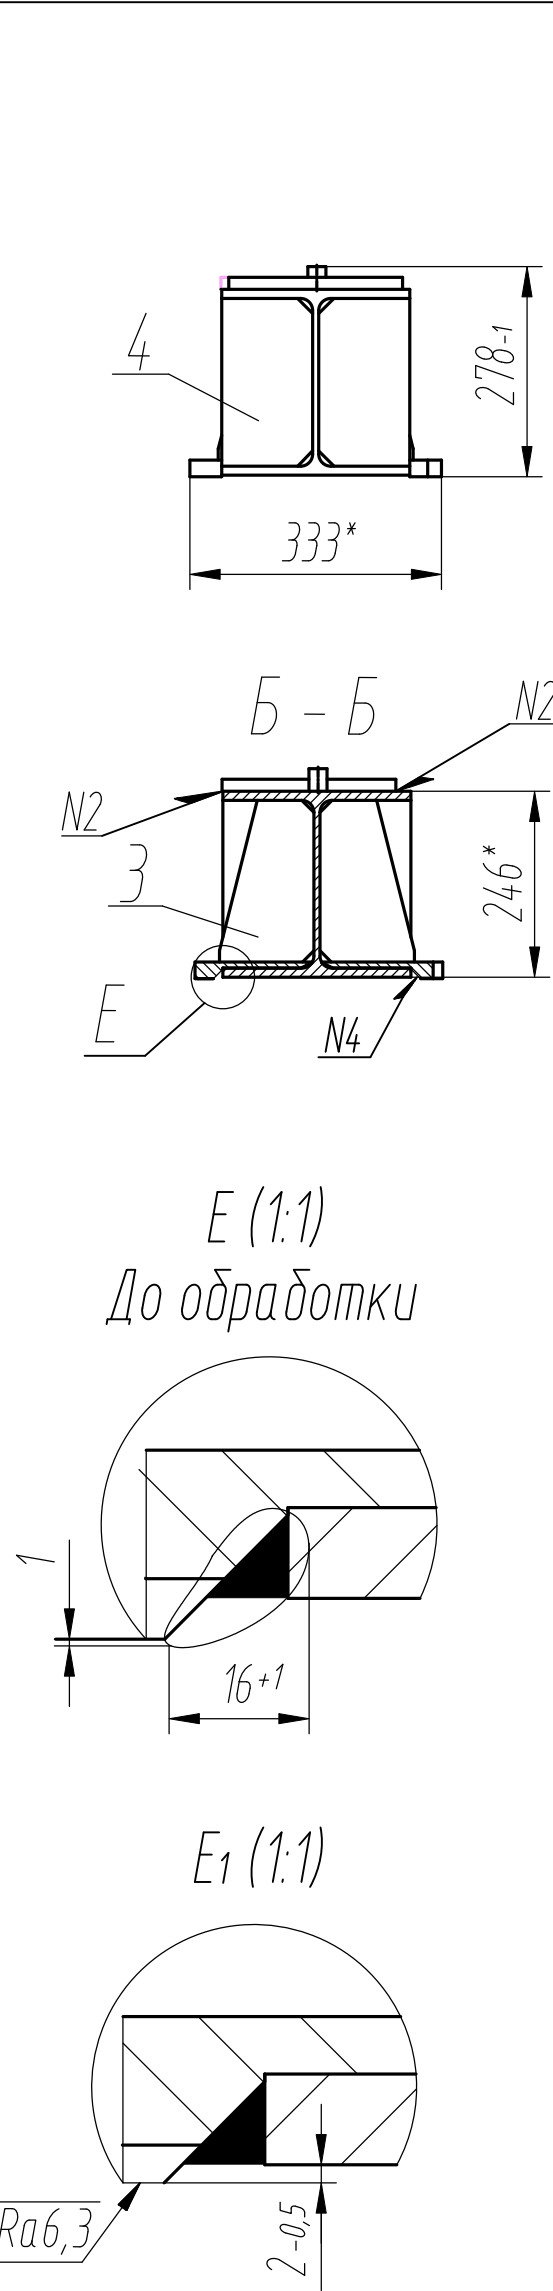
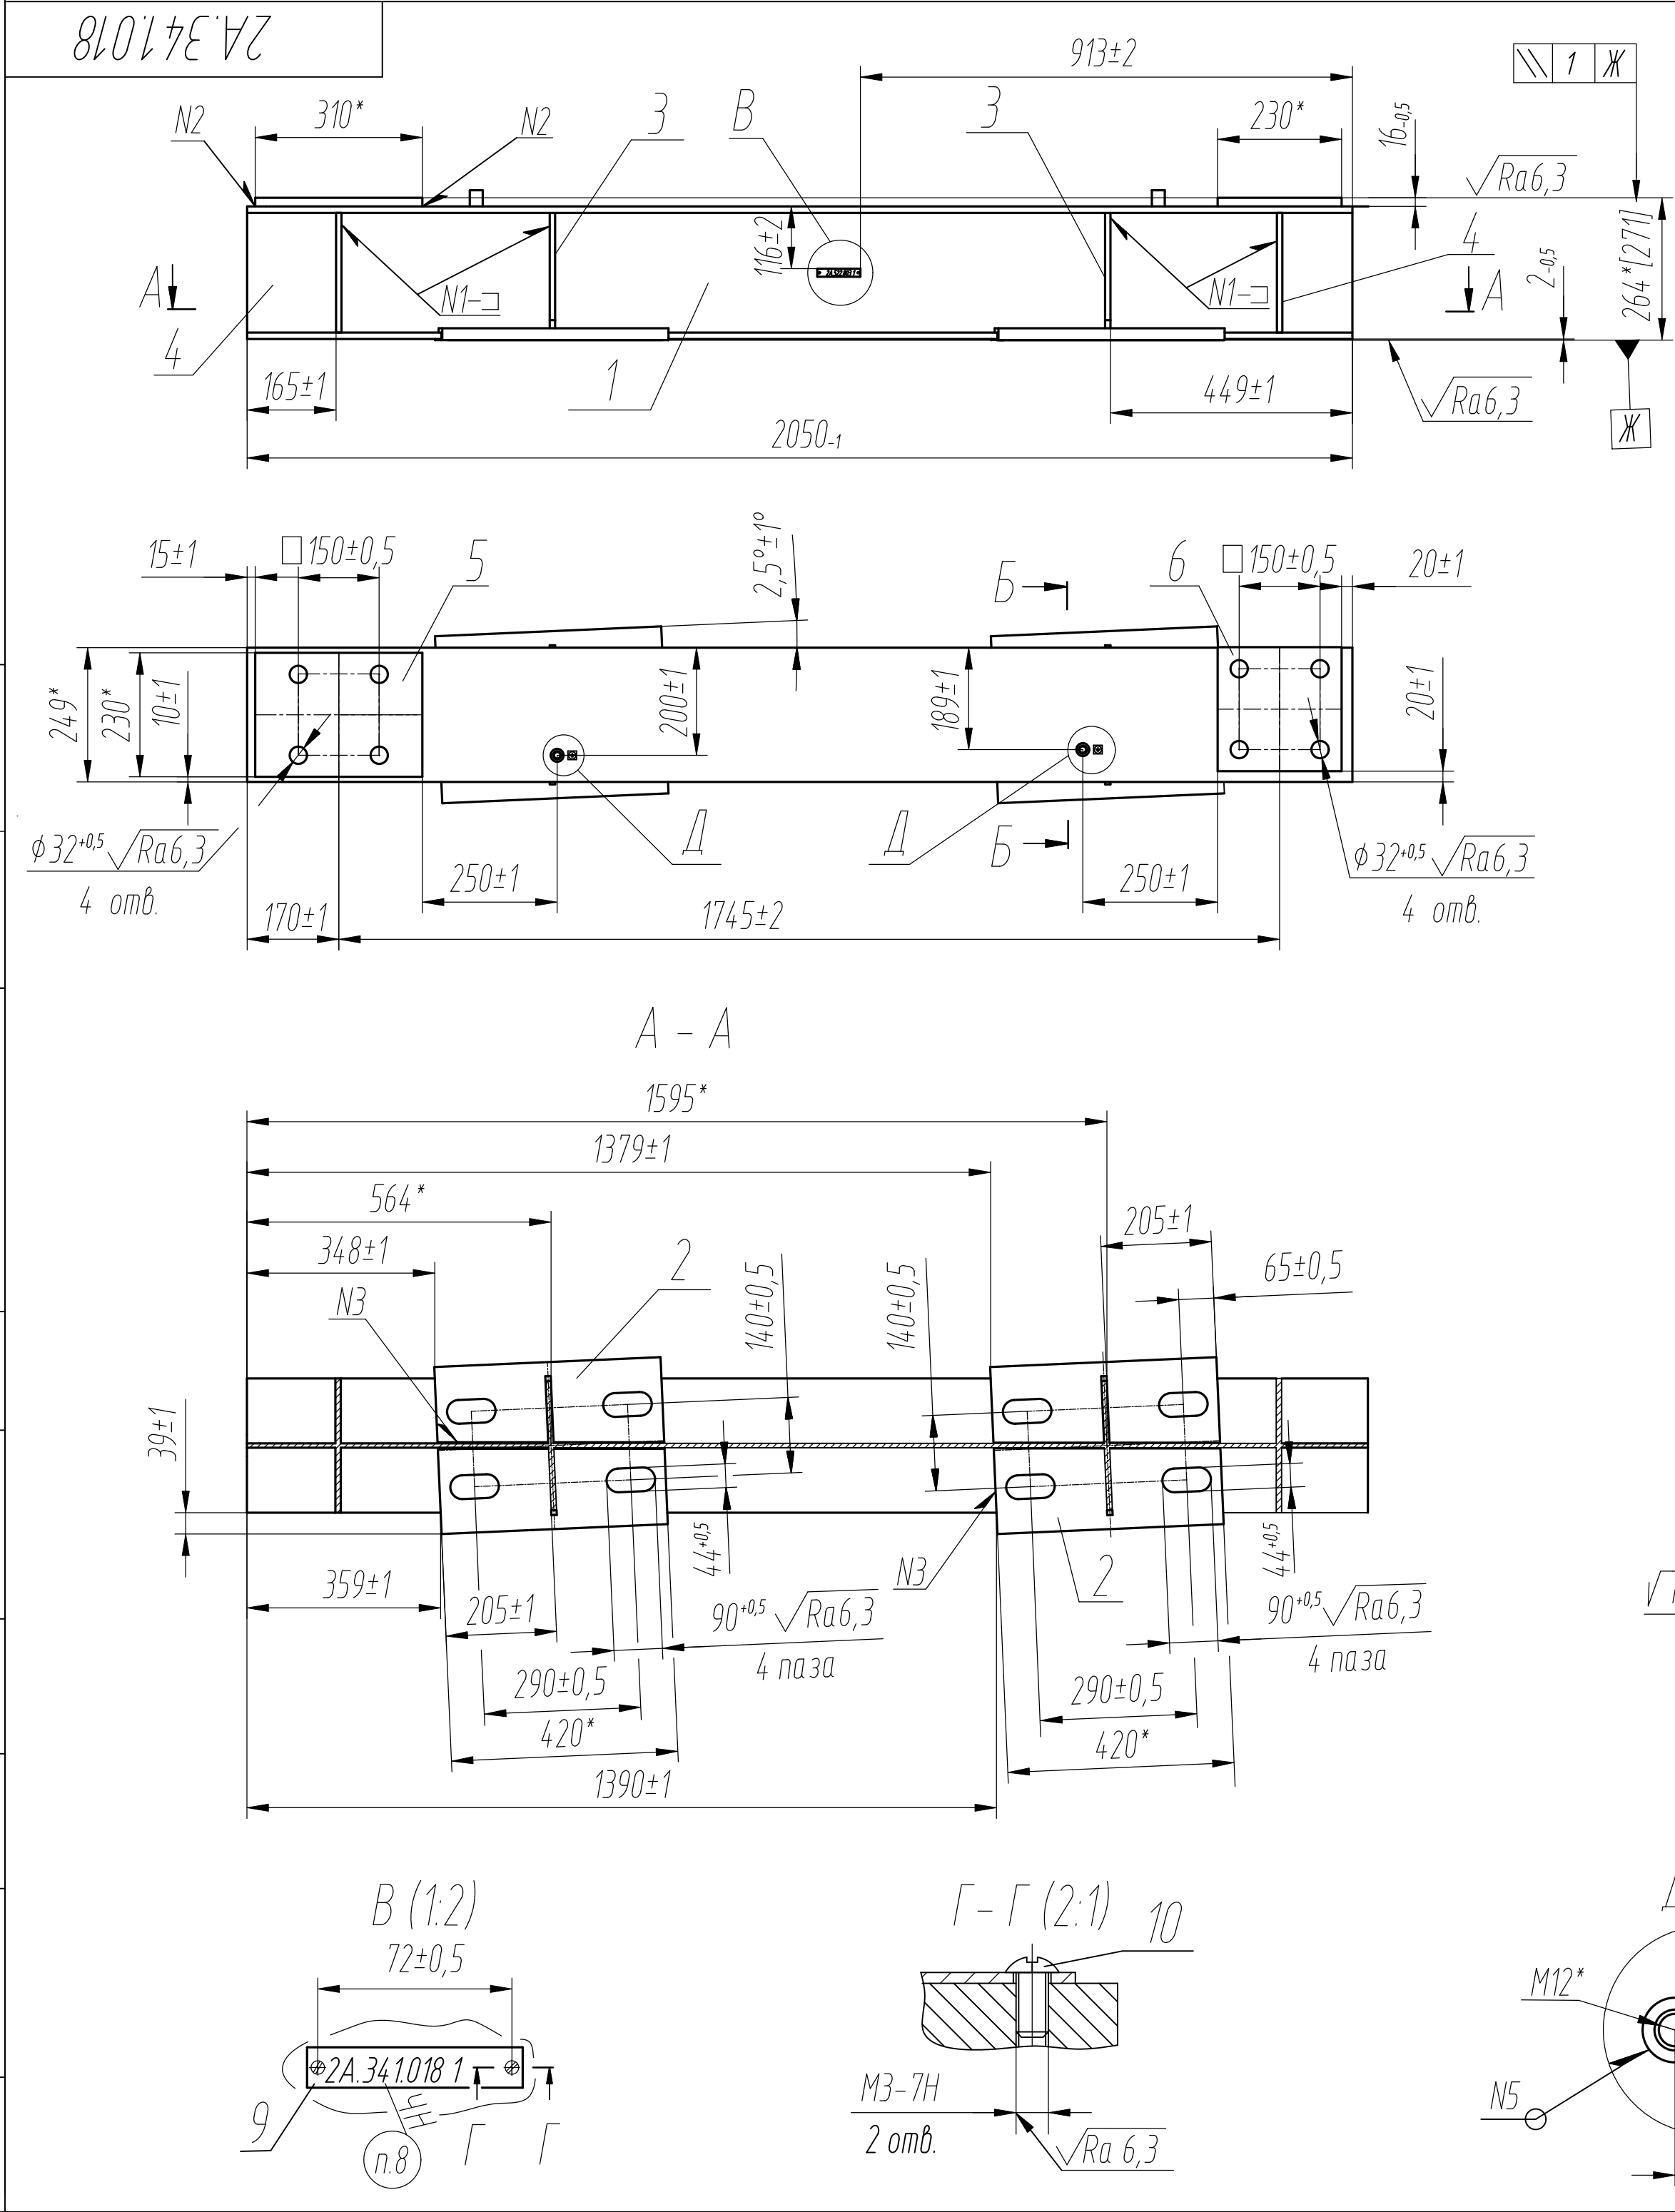


Таблица 1- Таблица сварных швов

Номер шва	Обозначение	Длина шва,м
N1	T3-△5	1,55
N2	H1-△5	1,96
N3	T1-△5	2,62
N4	см. вид Е	1,68
N5	T1-△3	0,16

- 1 Все материалы для сварки должны иметь сертификат.
- 2 Сварные швы выполнить сваркой в защитных газах по ГОСТ 14771-76, Сварочная проволока Св-08Г2С ГОСТ 2246-70
Длина сварных швов: см.Табл.1
- 3 Контроль качества:
- 100% N1-N5 визуальный осмотр по программе ПМ
Критерии приемки в соответствии с ГОСТ EN ISO 5817, уровень качества D/C.
Результаты контроля занести в протокол.
- 4 *Размеры для справок.
- 5 [] – размеры до обработки.
- 6 Покрытие (кроме контактных поверхностей бобышек зажимов заземления) – грунтровка ТЕМАСОАТ ГПЛ-С Прамер, белая, RAL9016,. Краска ТЕМАСОАТ RM40, серая RAL7001 III.Y1.
- 7 Оловянированную поверхность бобышек зажимов заземления поз.7 защитить от попадания брызг раскаленного металла (при сварке, краски и т.п.)
- 8 Маркировать на табличке поз.9 лазерным способом шрифтом 12-ПрЗ ГОСТ 26.008-85 обозначение изделия и идентификационный номер.
- 9 Знаки заземления поз.8 ставить на клей ВК-9 ТУ1-595-14-842-2004.
- 10 Строповку производить мягкими стропами, предохраняя изделие от повреждений.

						24.018.002 СБ		
Изм.	Лист	№ докум.	Подп.	Дата	Балка Сборочный чертеж	Лит.	Масса	Масштаб
							200	1:10
Разраб.	Лупкина					Лист	Листов	1
Пров.	Колесова					СПбГТУАП		
Т. контр.								
Н. контр.								
Утв.	Тимофеев							

Копировал

Формат А2