

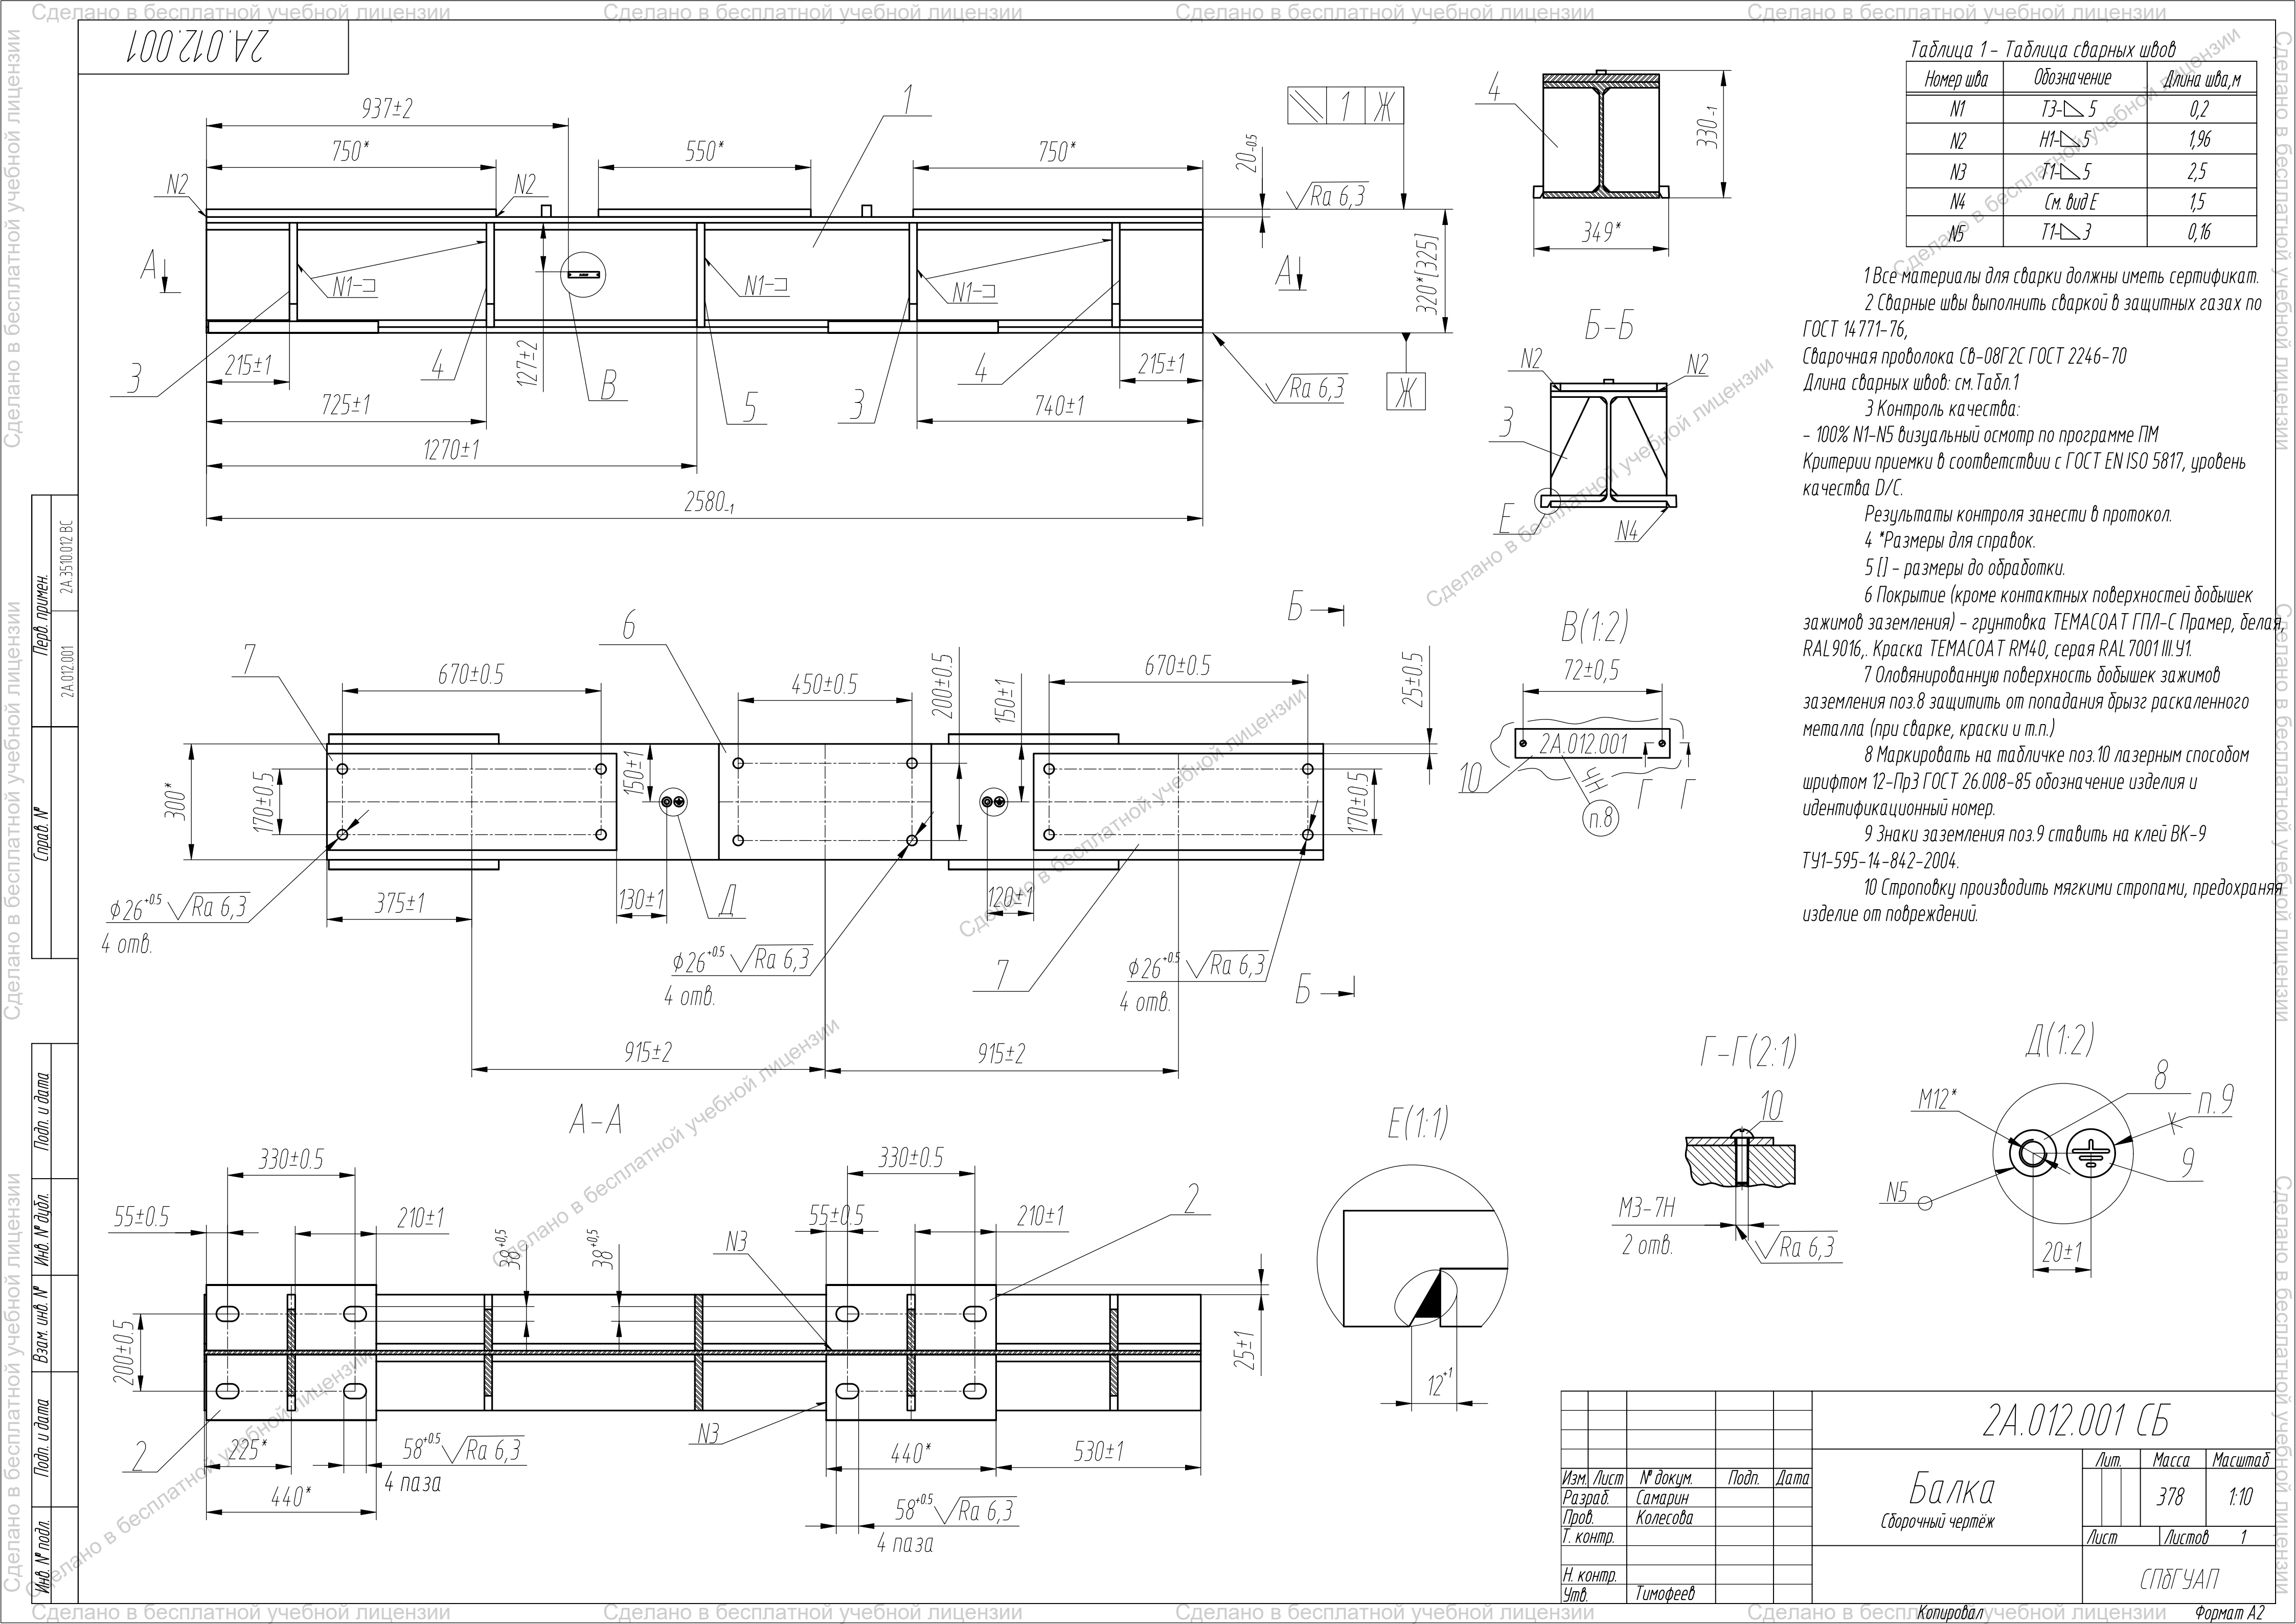
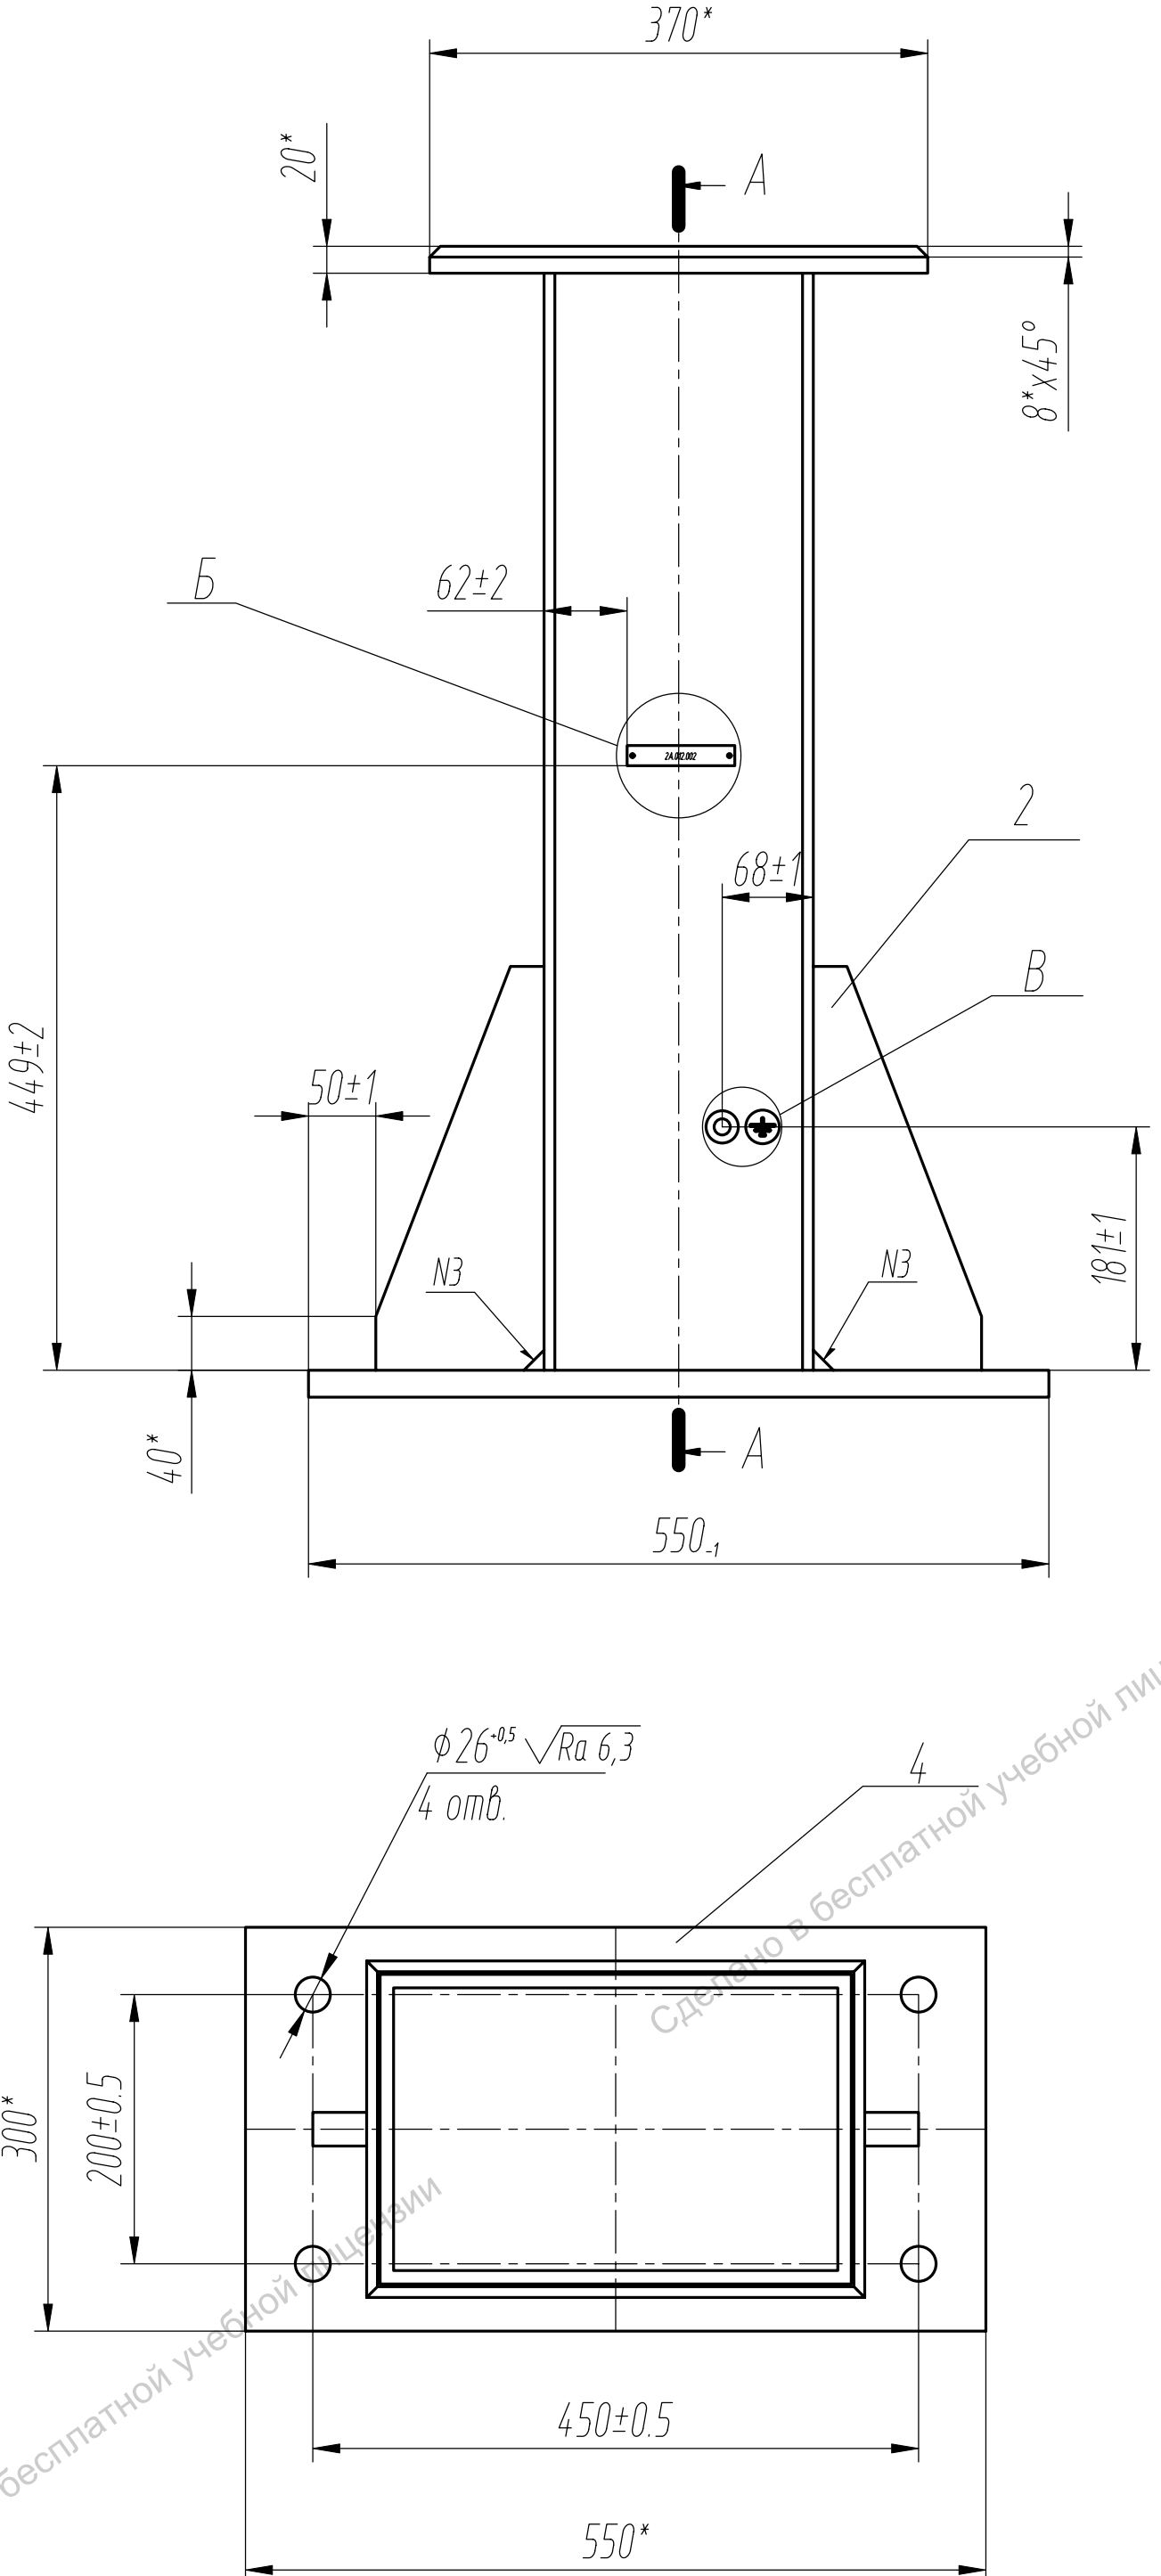


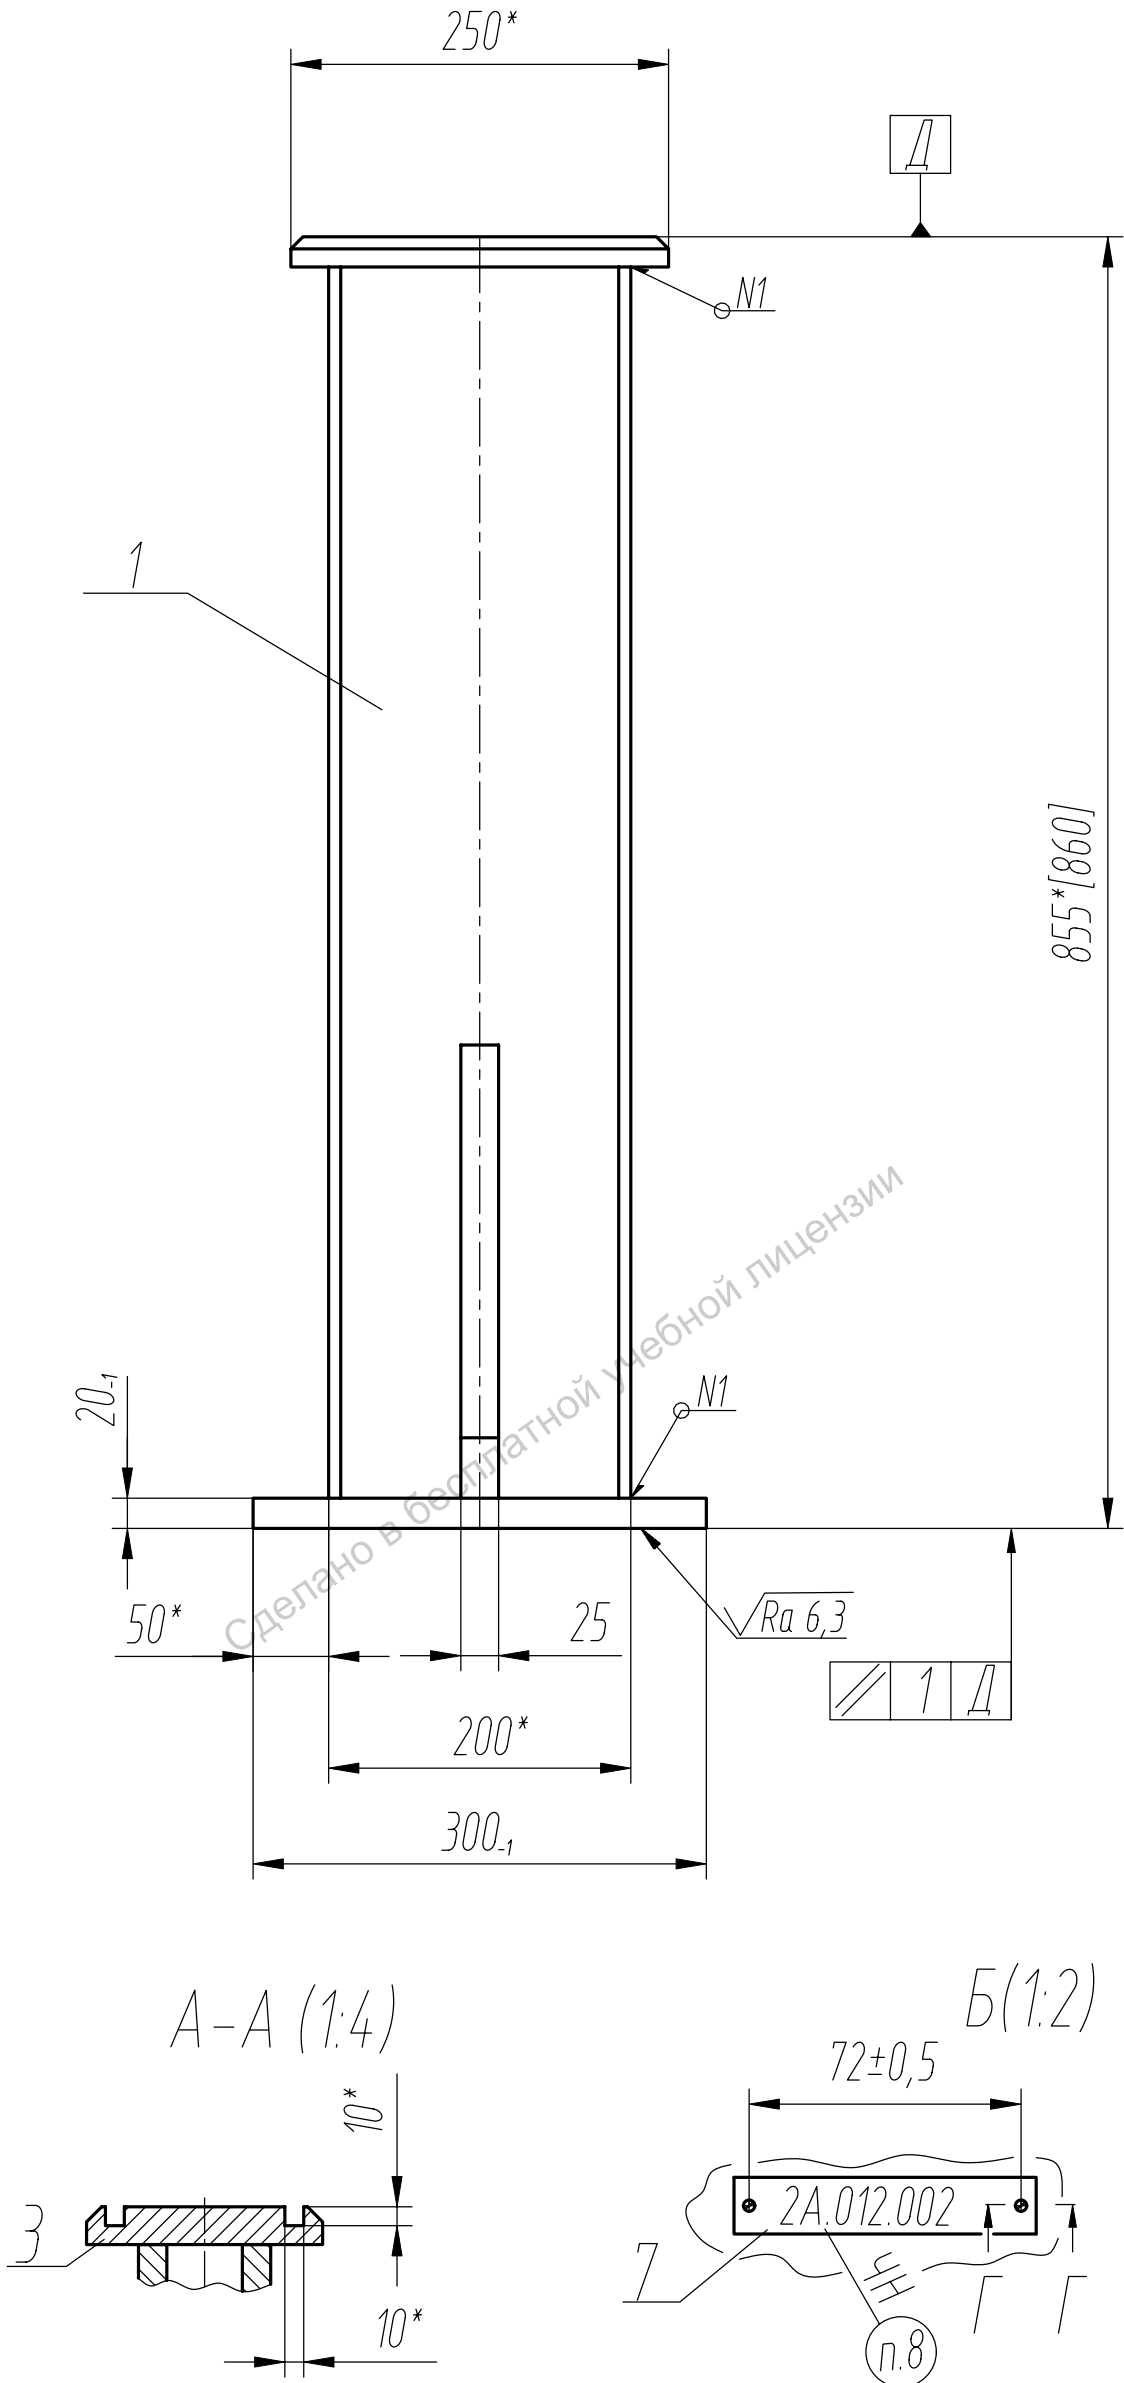

Номер шва	Обозначение	Длина шва, м
N1	T1-  5	0,2
N2	T1-  3	0,08
N3	T6	0,68

- 1 Все материалы для сварки должны иметь сертификат.
- 2 Сварные швы выполнить сваркой в защитных газах по ГОСТ 14771-76,
- Сварочная проволока Св-08Г2С ГОСТ 2246-70
- Длина сварных швов: см. Табл.1
- 3 Контроль качества:
 - 100% N1-N5 визуальный осмотр по программе ПМ
- Критерии приемки в соответствии с ГОСТ EN ISO 5817, уровень качества D/C.
- Результаты контроля занести в протокол.
- 4 *Размеры для справок.
- 5 [] – размеры до обработки.
- 6 Покрытие (кроме контактных поверхностей бобышек зажимов заземления) – грунтровка TEMACOAT ГПЛ-С Прамер, белая, RAL9016,. Краска TEMACOAT RM40, серая RAL7001 III.У1.
- 7 Оловянированную поверхность бобышек зажимов заземления поз.6 защитить от попадания брызг раскаленного металла (при сварке, краски и т.п.)
- 8 Маркировать на табличке поз.7 лазерным способом шрифтом 12-ПрЗ ГОСТ 26.008-85 обозначение изделия и идентификационный номер.
- 9 Знаки заземления поз.5 ставить на клей ВК-9 ТУ1-595-14-842-2004.
- 10 Строповку производить мягкими стропами, предохраняя изделие от повреждений.

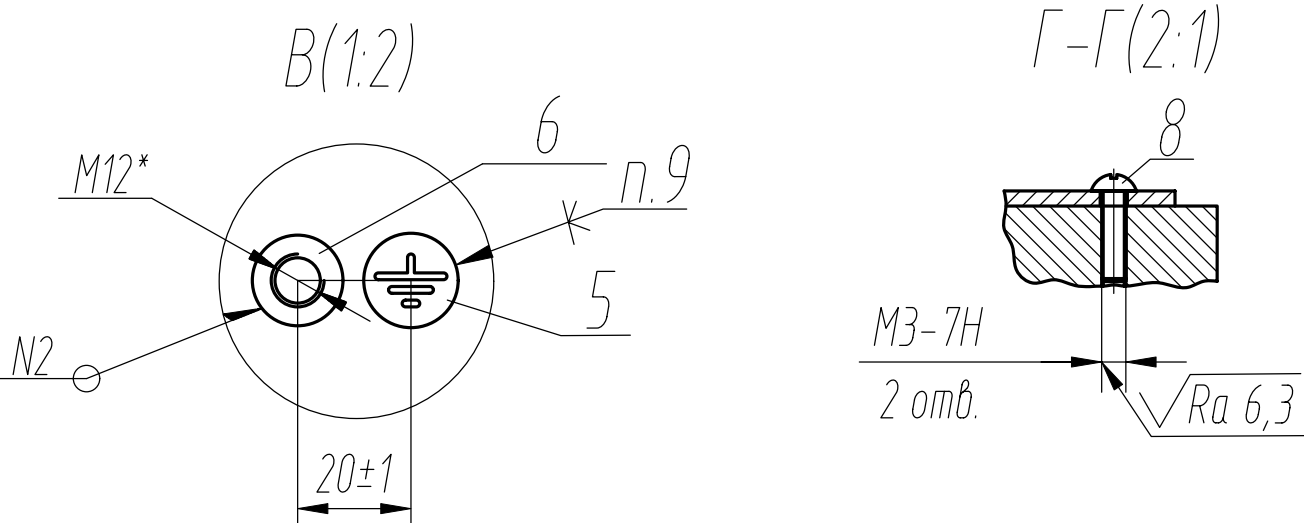

					2А.012.002 СБ			
					Подставка 1 Сборочный чертёж	Лист	Масса	Масштаб
Изм.	Лист	№ докум.	Подп.	Дата				
Разраб.		Самарин					65	1:5
Пров.		Колесова						
Т. контр.						Лист	Листов 1	
Н. контр.						СПбГУАП		
Утв.		Тимофеев						

2A.012.003






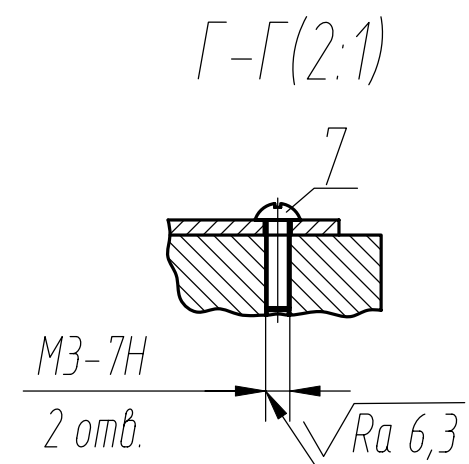


Таблица 1- Таблица сварных швов

Номер шва	Обозначение	Длина шва, м
N1	T1-5	0,2
N2	T1-3	0,08

- 1 Все материалы для сварки должны иметь сертификат.
- 2 Сварные швы выполнить сваркой в защитных газах по ГОСТ 14771-76, Сварочная проволока Св-08Г2С ГОСТ 2246-70
Длина сварных швов: см. Табл.1
- 3 Контроль качества:
 - 100% N1-N5 визуальный осмотр по программе ПМ
 - Критерии приемки в соответствии с ГОСТ EN ISO 5817, уровень качества D/C.
 - Результаты контроля занести в протокол.
- 4 *Размеры для справок.
- 5 [] - размеры до обработки.
- 6 Покрытие (кроме контактных поверхностей бобышек зажимов заземления) - грунтровка ТЕМАСОАТ ГПЛ-С Прамер, белая, RAL9016,. Краска ТЕМАСОАТ RM40, серая RAL 7001 III. У1.
- 7 Оловянированную поверхность бобышек зажимов заземления поз.6 защитить от попадания брызг раскаленного металла (при сварке, краски и т.п.)
- 8 Маркировать на табличке поз.7 лазерным способом шрифтом 12-ПрЗ ГОСТ 26.008-85 обозначение изделия и идентификационный номер.
- 9 Знаки заземления поз.5 ставить на клей ВК-9 ТУ1-595-14-842-2004.
- 10 Строповку производить мягкими стропами, предохраняя изделие от повреждений.

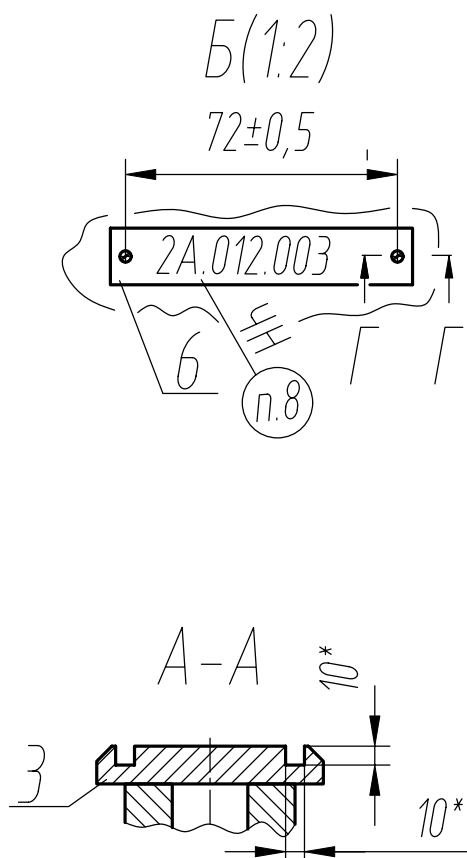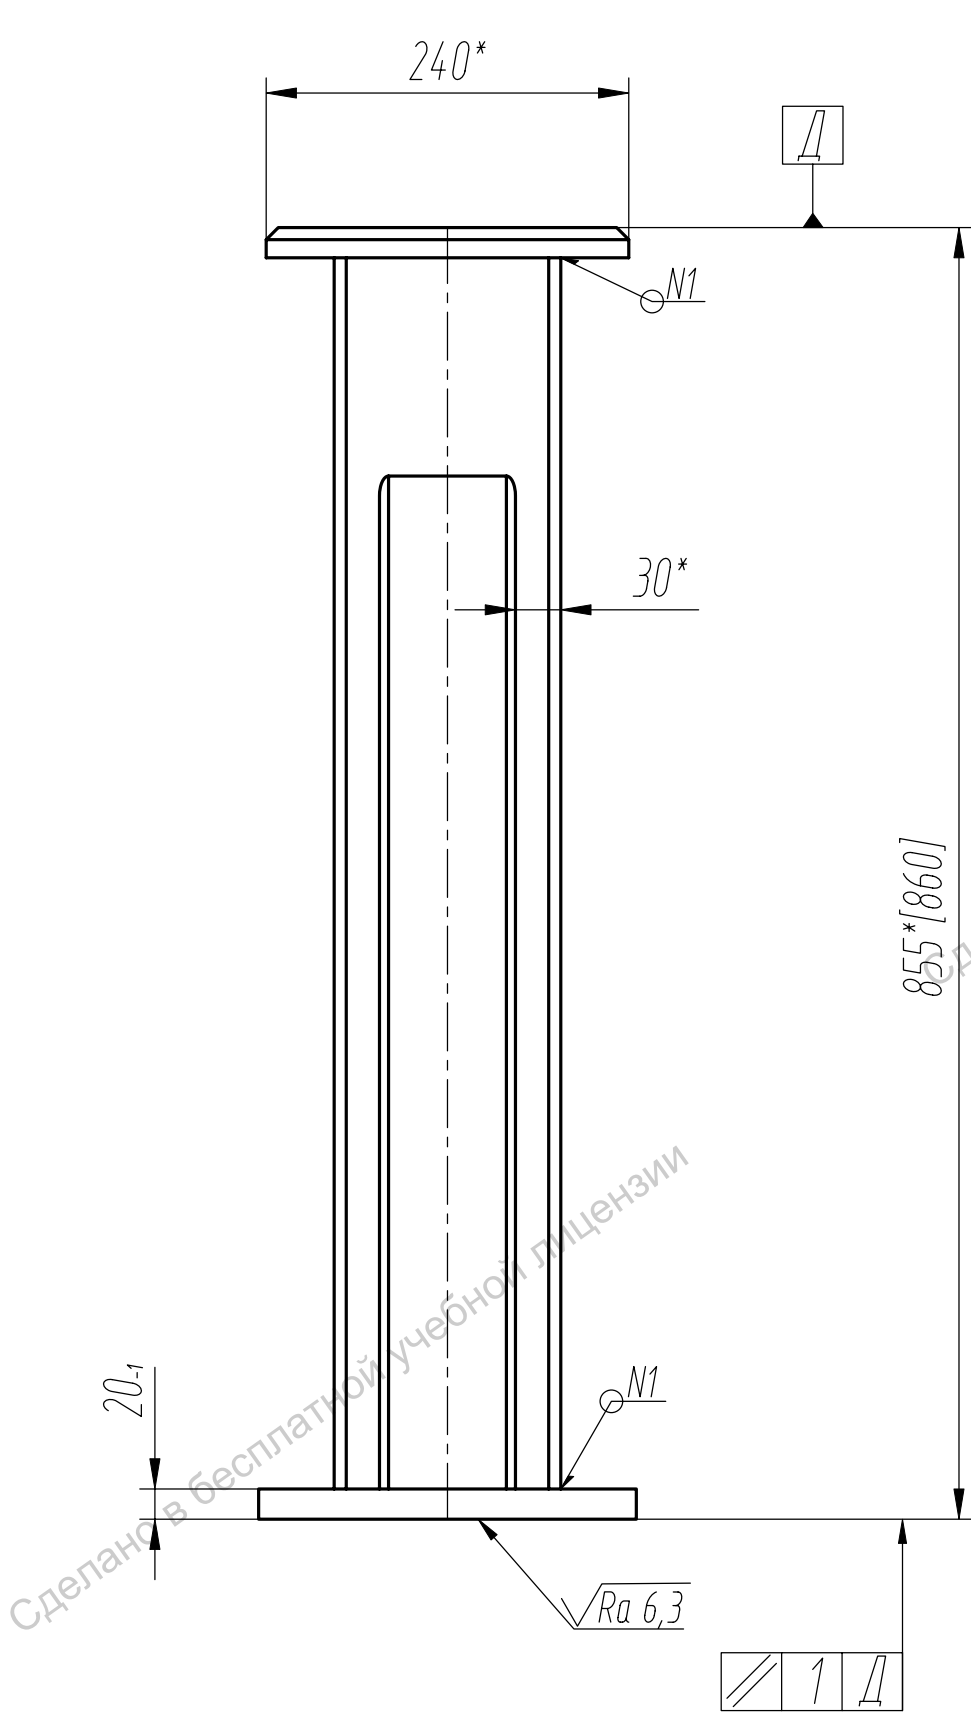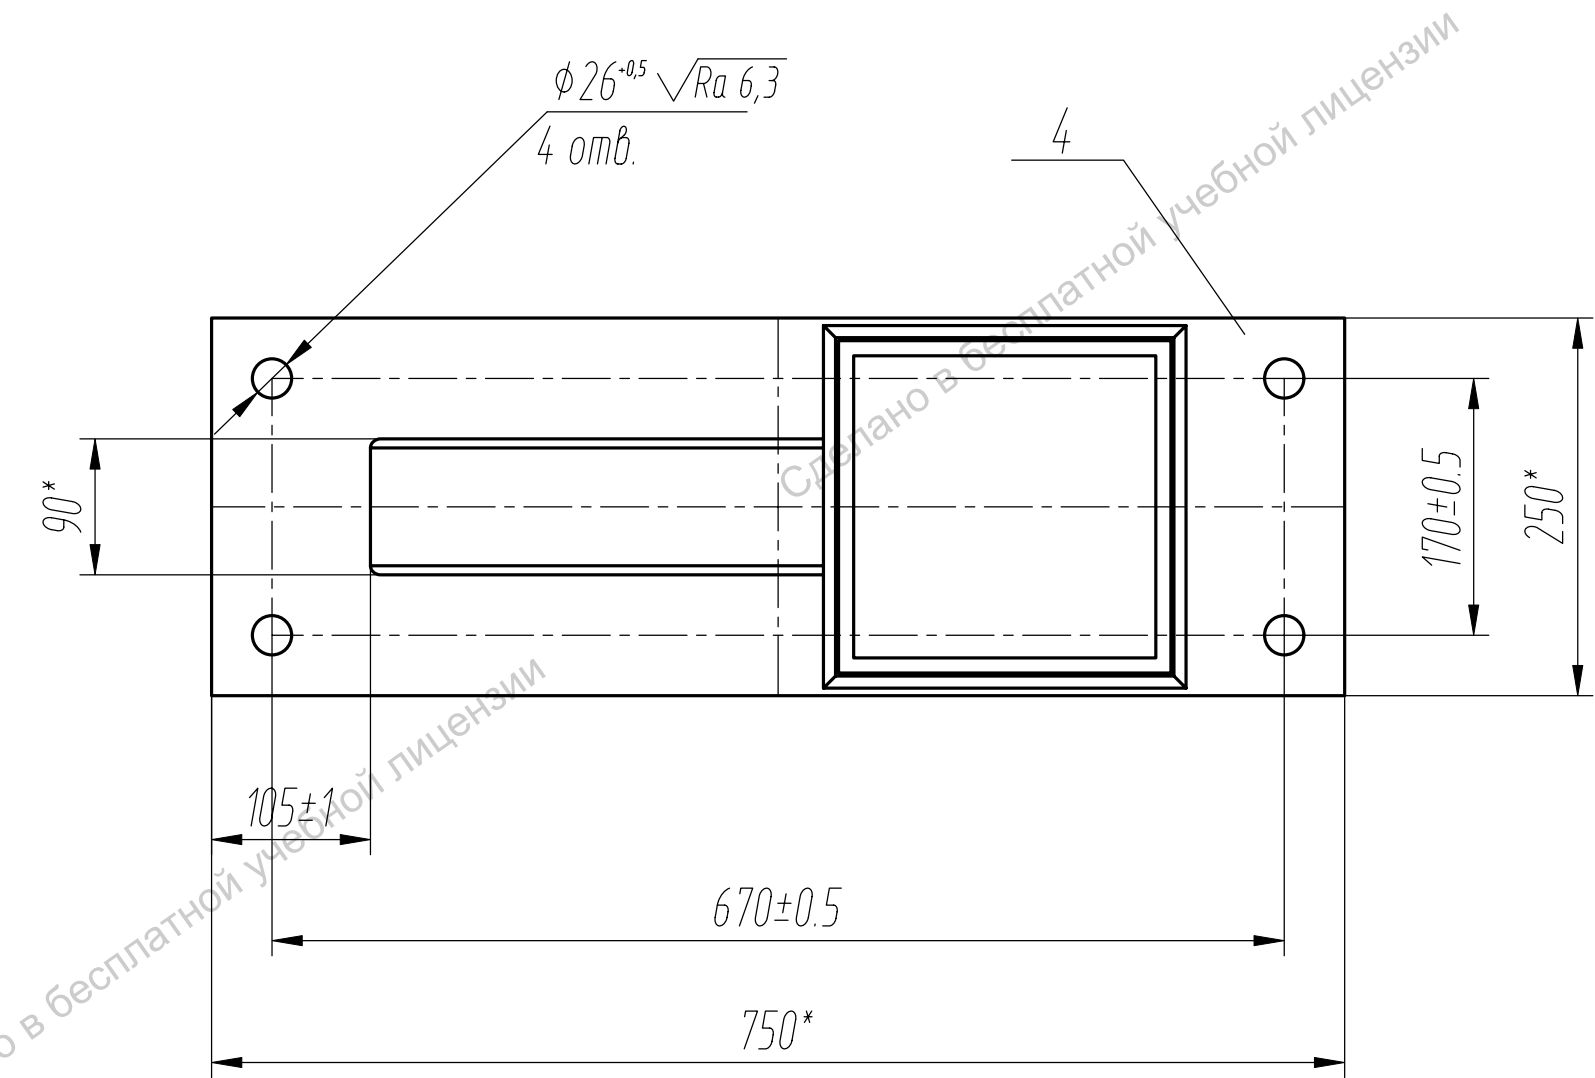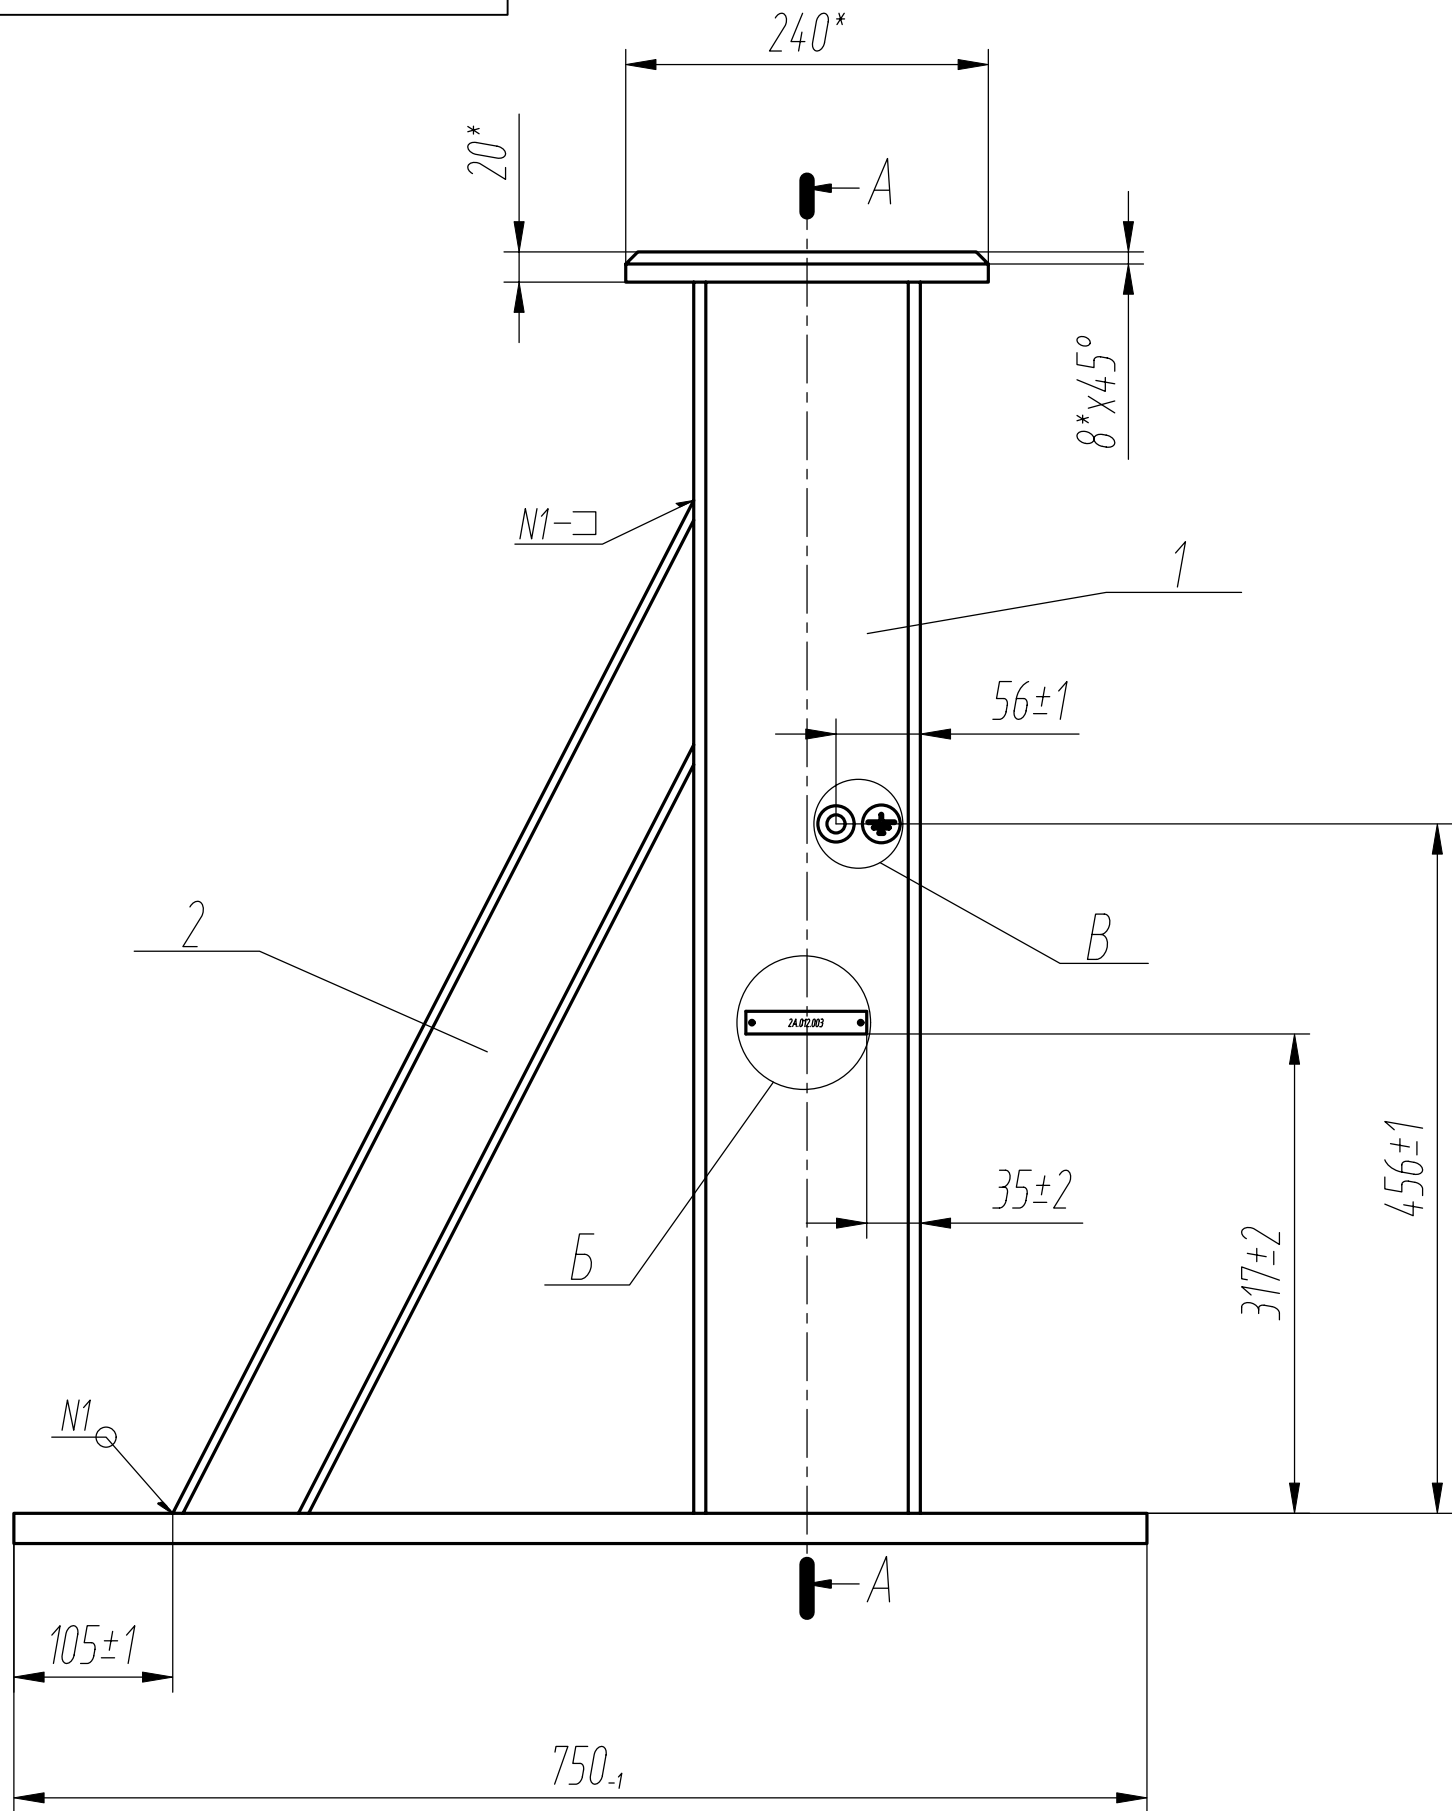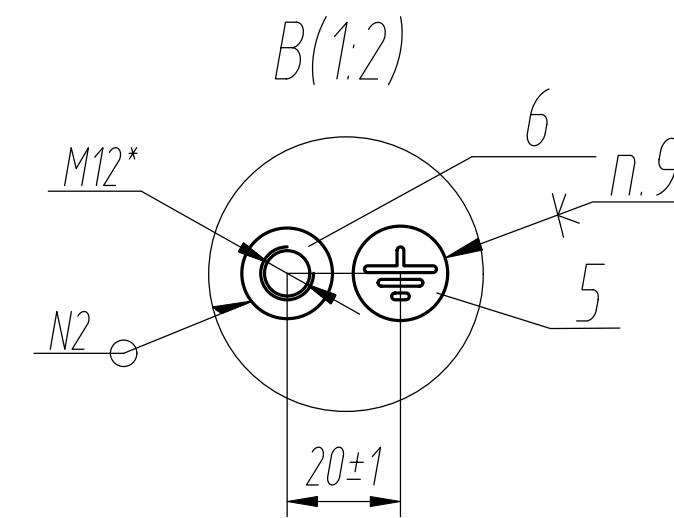

2A.012.003 СБ				Лит.	Масса	Масштаб
Подставка 2					54	1:5
Сборочный чертёж				Лист	Листов	1
СПбГУАП						